


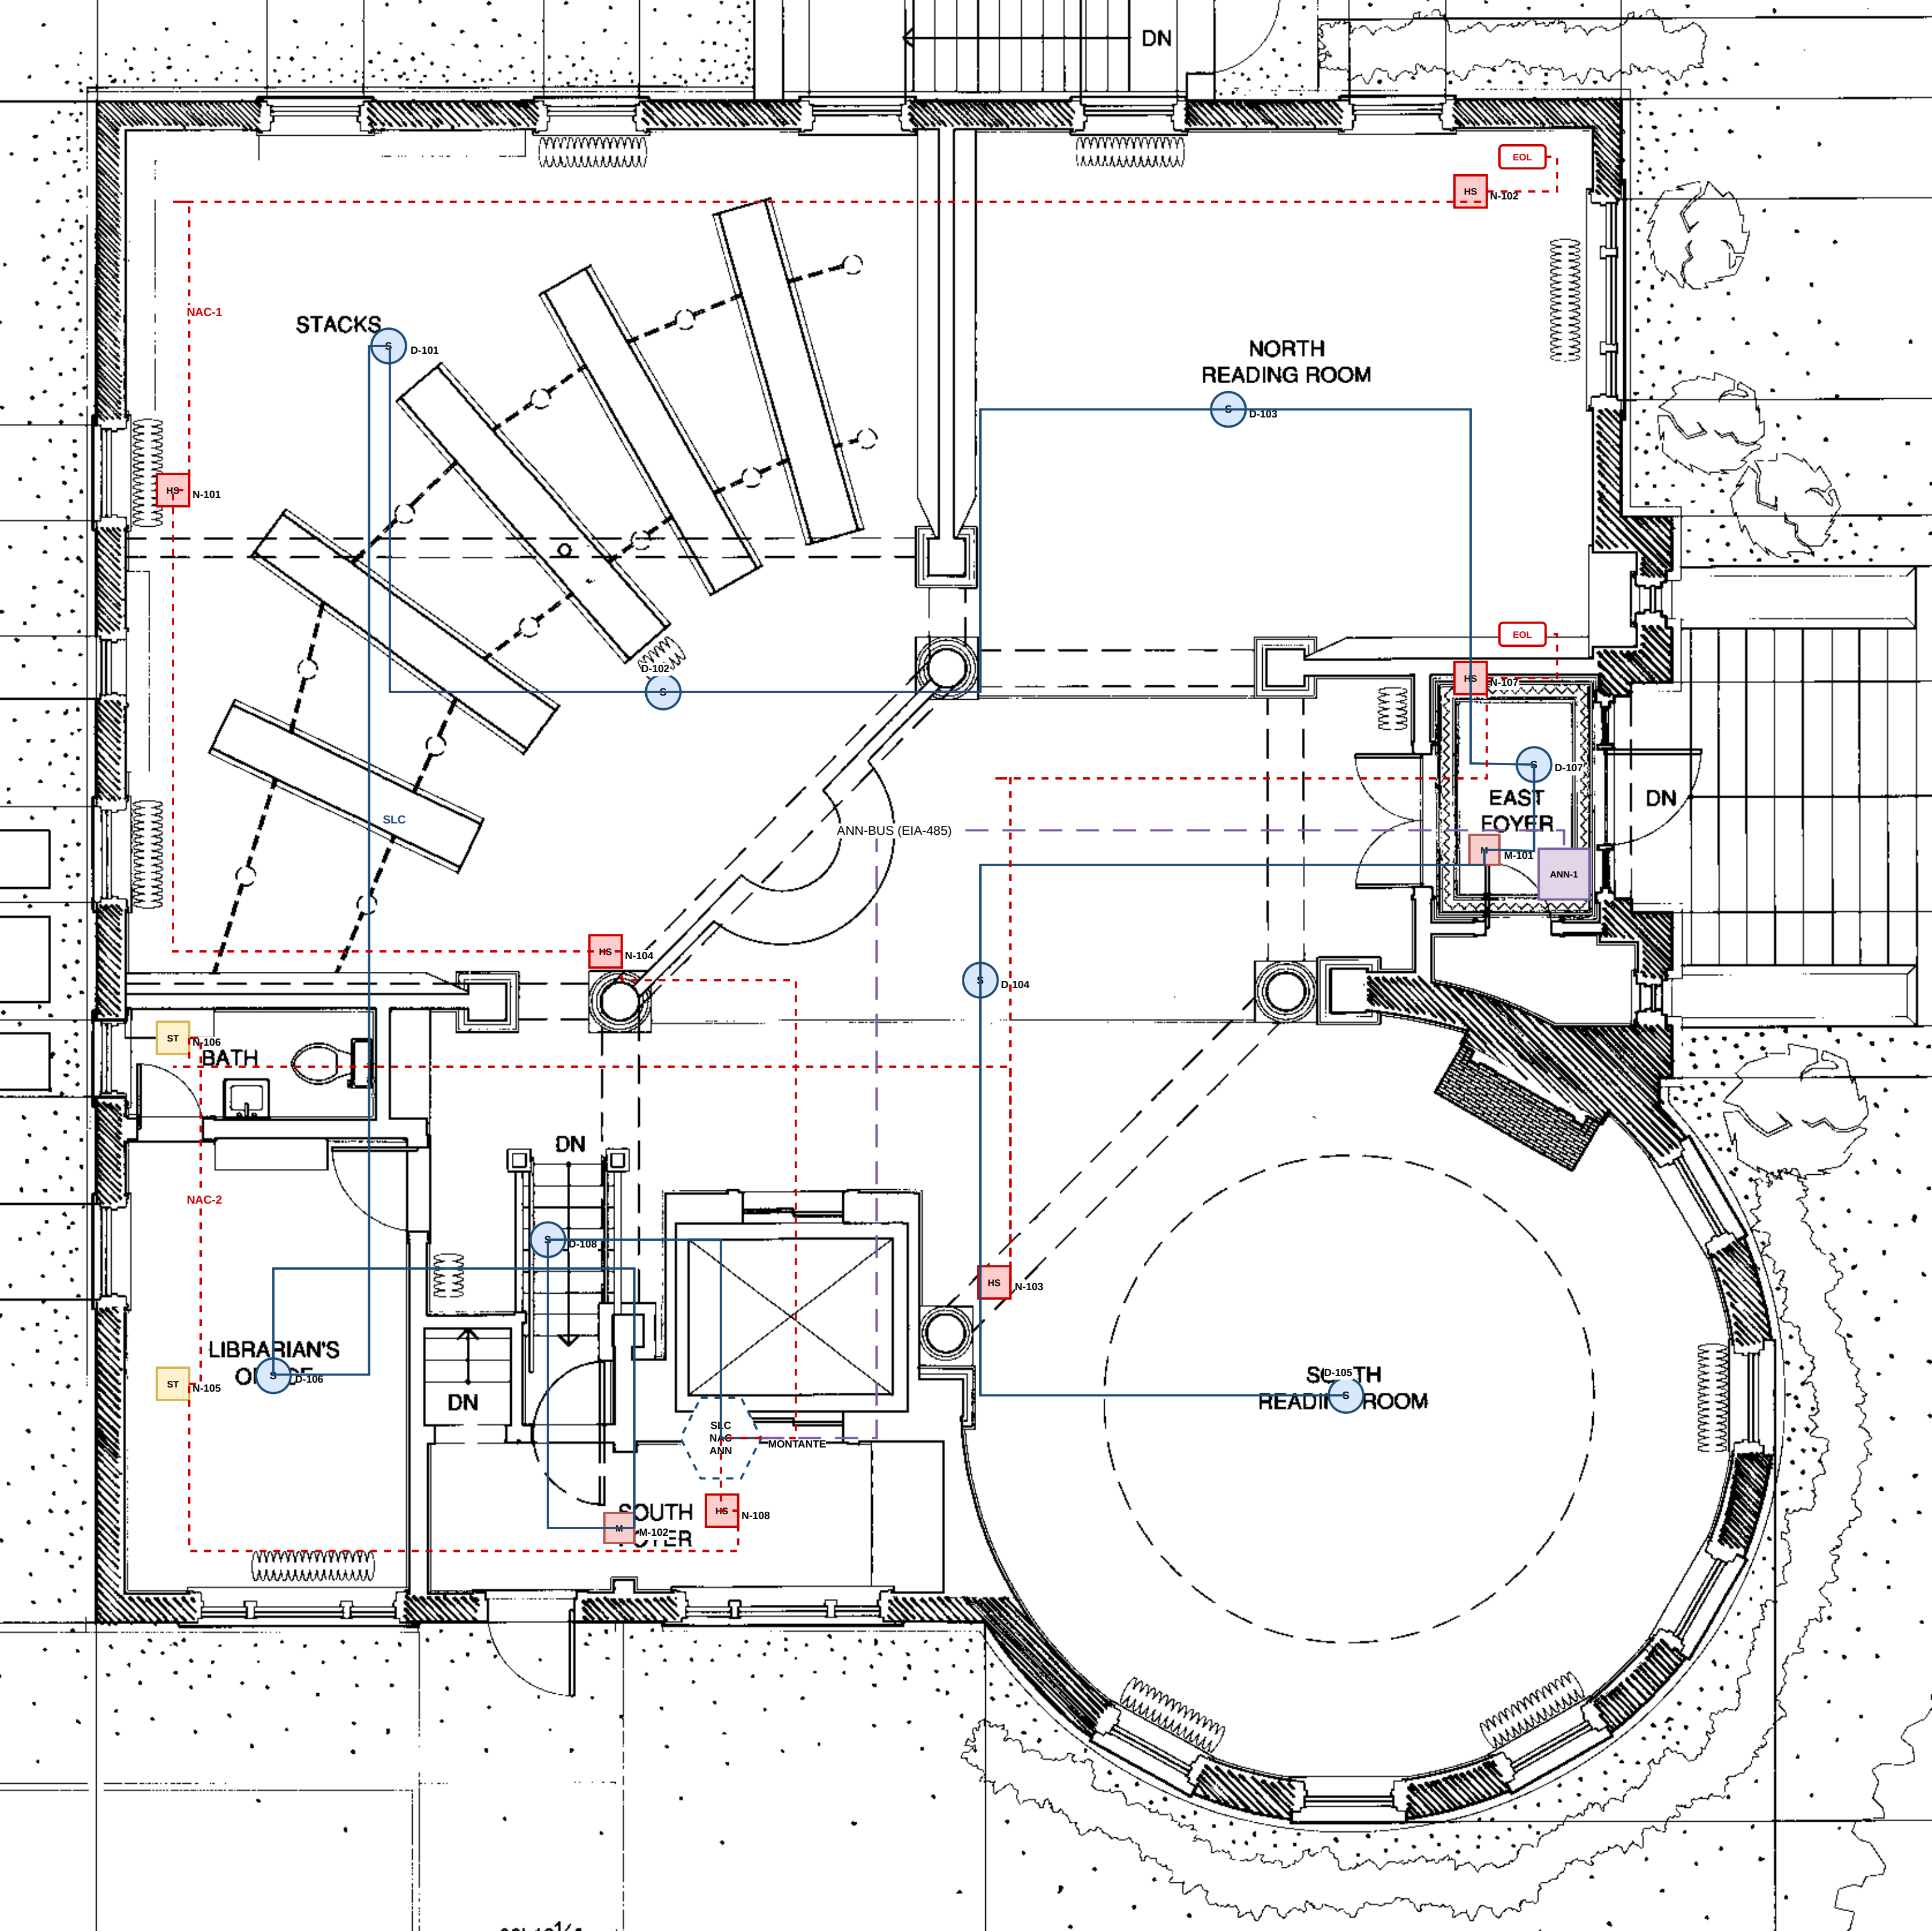

PISO 1 - Sistema de deteccion y alarma

Paxton Carnegie Library — 254 S. Market St, Paxton, Ford County, Illinois
Fondo: HAB5 IL-329, láminas 3 y 4, escala original 1/4"=1'-0" (comprobar con la escala gráfica impresa en el fondo)
Sistema Fire-Lite MS-9600LS direccionable — 1 lazo SLC Clase B (Style 4), 4 NAC Clase B (Style Y)

LEYENDA DE SIMBOLOS

-  Detector de humo direccionable SD355
-  Detector termico direccionable H355R
-  Estacion manual BG-12LX
-  Horn/Strobe System Sensor P2R
-  Strobe solo System Sensor SR
-  Anunciador remoto ANN-80
-  Panel de control Fire-Lite MS-9600LS
-  Montante entre niveles: lazo SLC + NAC + ANN-BUS
-  Resistencia de fin de línea NAC 4,7 kΩ ½ W (P/N 71252)

CIRCUITOS Y CRITERIO DE RECORRIDO

Línea continua azul = lazo SLC (detección direccionable, Clase B / Style 4)
Línea punteada roja = circuito NAC (notificación, Clase B / Style Y)
Línea punteada morada = ANN-BUS EIA-485 al anunciador ANN-80
Cada tramo lleva rótulo SLC / NAC-n sobre el recorrido.

El lazo SLC y los cuatro NAC ARRANCAN EN EL FACP (Electrical Room, sótano) y suben al piso 1 por el montante de la escalera del South Foyer, única conexión vertical interior del edificio.

Cada NAC Clase B termina en resistencia EOL de 4,7 kΩ ½ W (P/N 71252).
El lazo SLC Style 4 NO lleva EOL: se supervisa por comunicación (doc. 51309).


El cableado corre pegado a muros y por la circulación, y atraviesa tabiques sólo en los vanos de puerta. Los aparatos de notificación van montados SOBRE muro, con la lente entre 80 y 96 in del piso terminado (NFPA 72-2013 18.5.5.1), y destellan SINCRONIZADOS: los 4 NAC se programan con sincronización tipo System Sensor en el panel (manual 52646:B, §3.6.5.5.8); no hace falta MDL3.



NORTE según la lámina HAB5 original.
El plano se dibuja con el norte hacia arriba.

PROYECTO: Sistema de detección y alarma contra incendios
EDIFICIO: Paxton Carnegie Library – 254 S. Market St, Paxton, Ford Co., Illinois
CURSO: EL-4601 Normalización Técnica para Electrónica – Proyecto No. 1
NORMAS: NFPA 72-2013 · NFPA 101-2015 · NEC (NFPA 70) Art. 760 · UL 864

LÁMINA: 1 de 3 – PLANTA PISO 1
ESCALA: fondo a 1/4"=1'-0" (lámina HAB5 4) – verificar al imprimir
REVISIÓN: B – FECHA: _____
AUTORES: _____

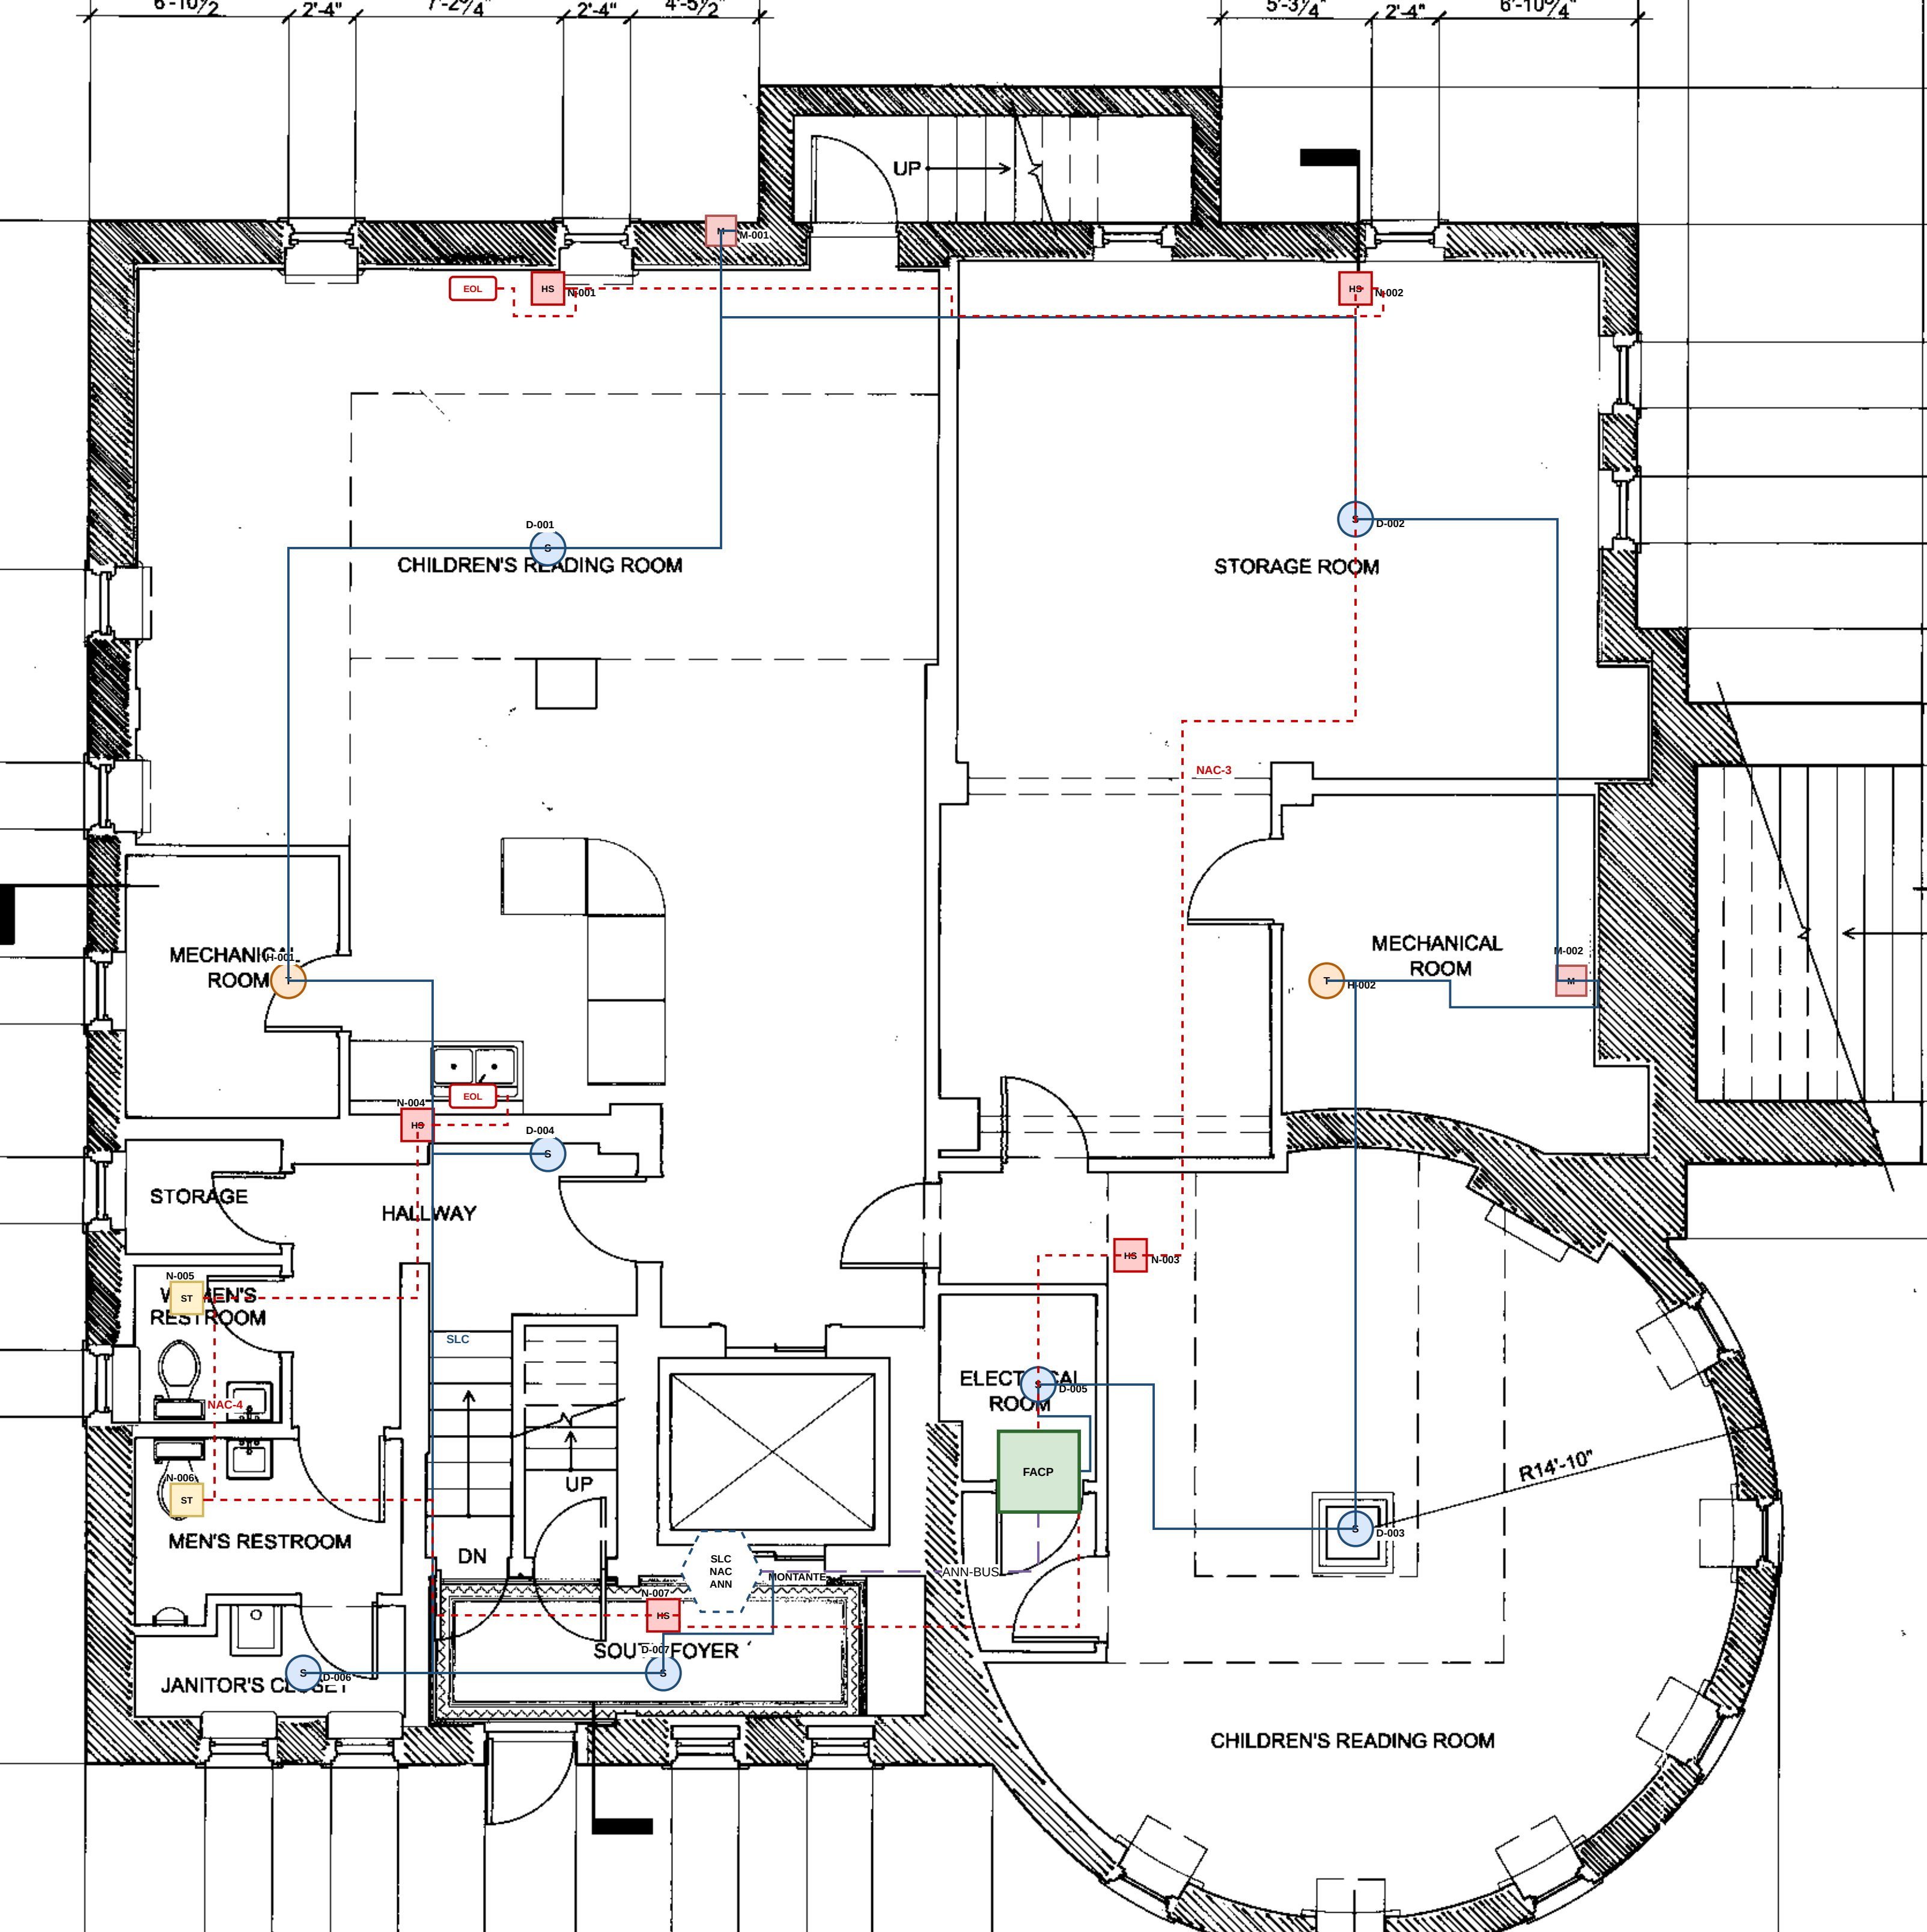

SOTANO - Sistema de deteccion y alarma

Paxton Carnegie Library — 254 S. Market St, Paxton, Ford County, Illinois
Fondo: HABS IL-329, láminas 3 y 4, escala original 1/4"=1'-0" (comprobar con la escala gráfica impresa en el fondo)
Sistema Fire-Lite MS-9600LS direccionable — 1 lazo SLC Clase B (Style 4), 4 NAC Clase B (Style Y)

LEYENDA DE SIMBOLOS

- Detector de humo direccionable SD355
- Detector termico direccionable H355R
- Estacion manual BG-12LX
- Horn/Strobe System Sensor P2R
- Strobe solo System Sensor SR
- Anunciador remoto ANN-80
- Panel de control Fire-Lite MS-9600LS
- Montante entre niveles: lazo SLC + NAC + ANN-BUS
- Resistencia de fin de línea NAC 4,7 kΩ ½ W (P/N 71252)

CIRCUITOS Y CRITERIO DE RECORRIDO

Línea continua azul = lazo SLC (detección direccionable, Clase B / Style 4)
Línea punteada roja = circuito NAC (notificación, Clase B / Style Y)
Línea punteada morada = ANN-BUS EIA-485 al anunciador ANN-80
Cada tramo lleva rótulo SLC / NAC-n sobre el recorrido.

El lazo SLC y los cuatro NAC ARRANCAN EN EL FACP (Electrical Room, sótano) y suben al piso 1 por el montante de la escalera del South Foyer, única conexión vertical interior del edificio.

Cada NAC Clase B termina en resistencia EOL de 4,7 kΩ ½ W (P/N 71252).
El lazo SLC Style 4 NO lleva EOL: se supervisa por comunicación (doc. 51309).

El cableado corre pegado a muros y por la circulación, y atraviesa tabiques sólo en los vanos de puerta. Los aparatos de notificación van montados SOBRE muro, con la lente entre 80 y 96 in del piso terminado (NFPA 72-2013 18.5.5.1), y destellan SINCRONIZADOS: los 4 NAC se programan con sincronización tipo System Sensor en el panel (manual 52646:B, §3.6.5.5.8); no hace falta MDL3.



NORTE según la lámina HABS original.
El plano se dibuja con el norte hacia arriba.

PROYECTO: Sistema de detección y alarma contra incendios
EDIFICIO: Paxton Carnegie Library — 254 S. Market St, Paxton, Ford Co., Illinois
CURSO: EL-4601 Normalización Técnica para Electrónica — Proyecto No. 1
NORMAS: NFPA 72-2013 · NFPA 101-2015 · NEC (NFPA 70) Art. 760 · UL 864

LÁMINA: 2 de 3 — PLANTA SÓTANO
ESCALA: fondo a 1/4"=1'-0" (lámina HABS 3) — verificar al imprimir
REVISIÓN: B — FECHA: _____
AUTORES: _____

ALIMENTACION DEL FACP (Electrical Room, sótano)
ACOMETIDA 120 VAC, 3,0 A - circuito derivado DEDICADO, rotulado "FIRE ALARM", 14 AWG / 600 V - NEC Art. 760, sin dispositivos de desconexion en el recorrido.
RESPALDO: 2 x batería sellada 12 V / 12 AH en serie (24 VDC, 12 AH).

Paxton Carnegie Library - 254 S. Market St, Paxton, Ford County, Illinois | HABS IL-329
Sistema Fire-Lite MS-9600LS direccionable | Seccion 5.2 | Diagrama sin escala

